ASSEMBLAGES TYPIQUES

P1 — RF: 60 MIN. ULC
PLANCHER –P1–
FINI DE PLANCHER (PROPR.)
BÉTON LÉGER 1.5 po.
COUSSIN CAOUTCHOUC
C.P. 5/8" COLLÉ/FIXÉ
SOLIVES DE PLANCHER
PRÉFABRIQUÉES 12" NOM.
AVEC LAINE ROXUL 4"
BARRES RÉSILIENTES
2 X GYPSE 5/8" TYPE "X"

P2
PLANCHER –P2–
FINI DE PLANCHER
(PROPRIÉTAIRE)
C.P. 5/8" COLLÉ/FIXÉ
FOURRURES 2" X 3" @ 16"
À PLAT
DALLE DE BÉTON ARMÉE
PARE–VAPEUR 6 MILS
STYROFOAM SM 1 po.
CONCASSÉ EXEMPT DE
PYRITE
SOL NATUREL SAIN

M1
MUR –M1– (BRIQUES)
PAREMENT DE BRIQUES
ESPACE D'AIR 1"
MEMBRANE TYVEK
AGGLOMÉRÉ 7/16" AVEC
ISOLANT RIGIDE R4.
MONTANTS 2" X 6" @ 16"
C/C AVEC ISOLANT R20
PARE–VAPEUR 6 MILS
FOURRURES 1" X 3" @
16"C/C
GYPSE 5/8" TYPE "X"

M3
MUR –M3– FONDATION
GYPSE 5/8" F.C.
PARE–VAPEUR 6 MILS
MONTANTS 2" X 4" @ 16"
C/C AVEC LAINE R12
ISOLANT RIGIDE 1 po.
MUR DE BÉTON 10" OU 8"
IMPERMÉABILISÉ SOUS LE
SOL
ARMÉ 2 BARRES 10M HAUT
+ BAS DU MUR (VOIR ING.
TOUT LE PÉRIMÈTRE)

P — PORTE D'ENTRÉE LOGEMENTS
PORTE 20 MINUTES ULC
AVEC FERME–PORTES

M2 — RF: 45 MIN. ULC
MUR –M2– (BARDAGE)
PAREMENT "CANEXEL"
FOURRURES DE BOIS 1"
MEMBRANE TYVEK
AGGLOMÉRÉ 7/16" AVEC
ISOLANT RIGIDE 1 po.
MONTANTS 2" X 6" @ 16"
C/C AVEC ISOLANT R20
PARE–VAPEUR 6 MILS
FOURRURES 1" X 3" @
16"C/C
GYPSE 5/8" TYPE "X"

C1 — RF: 45 MIN. ULC
CLOISON –C1– CLOISONS PORTANTE
GYPSE 5/8" TYPE "X" F.C.
MONTANTS 2" X 4" @ 12"/16" C/C
AVEC LAINE ROXUL
GYPSE 5/8" TYPE "X" FC

C2 — RF: 60 MIN. ULC
CLOISON –C2– CLOISONS ESCALIER
2 X GYPSE 5/8" TYPE "X" F.C.
MONTANTS 2" X 4" @ 12"/16" C/C
AVEC LAINE ROXUL
BARRES RÉSILIENTES ¾"
GYPSE 5/8" TYPE "X" FC

T1 — RF: 45 MIN. ULC
TOIT –T1–
BARDEAUX D'ASPHALTE 25
ANS SUR MEMBRANE
SOUS–COUCHE COLLÉE
SOPREMA
C.P. 5/8"
FERMES DE TOITURE
PRÉFABRIQUÉES AVEC ISOLANT
R40
NB: ENTRETOIT À VENTILER
AVEC DES AÉRATEURS
"MAXIMUM"
PARE–VAPEUR 6 MILS
FOURRURES 1" X 3" @ 16"C/C
1 X GYPSE 5/8" TYPE "X"

T2
TOIT –T2–
MEMBRANE ÉLASTOMÈRE
SOPREMA
SOUS–COUCHE (BASE) SOPREMA
C.P. 3/4" EMBOUVETÉ
POUTRELLES DE TOITURE
PRÉFABRIQUÉES
NB: ENTRETOIT À VENTILER PAR
EN DESSOUS
FOURRURES DE BOIS
SOFFITE (VENTILÉ)

C3 — RF: 60 MIN. ULC
CLOISON –C3– DOUBLE
GYPSE 5/8" TYPE "X" FC
BARRES RÉSILIENTES
MONTANTS 2" X 6" @ 12"/16" C/C
AVEC LAINE INSONORISANTE
ESPACE D'AIR 3/4"
MONTANTS 2" X 4" @ 12"/16" C/C
AVEC LAINE INSONORISANTE
BARRES RÉSILIENTES
GYPSE 5/8" TYPE "X" FC

Type C2	34.7 FT
Type M2	75.9 FT
Type M1	75.8 FT
Type C1	111.3 FT
Ceiling Type T1	1,201.4 SQ FT
Ceiling Type T1 - MR	133.7 SQ FT
Paint walls	364.9 FT
Interior doors	7.0
Sliding door	3.0
Exterior doors	1.0

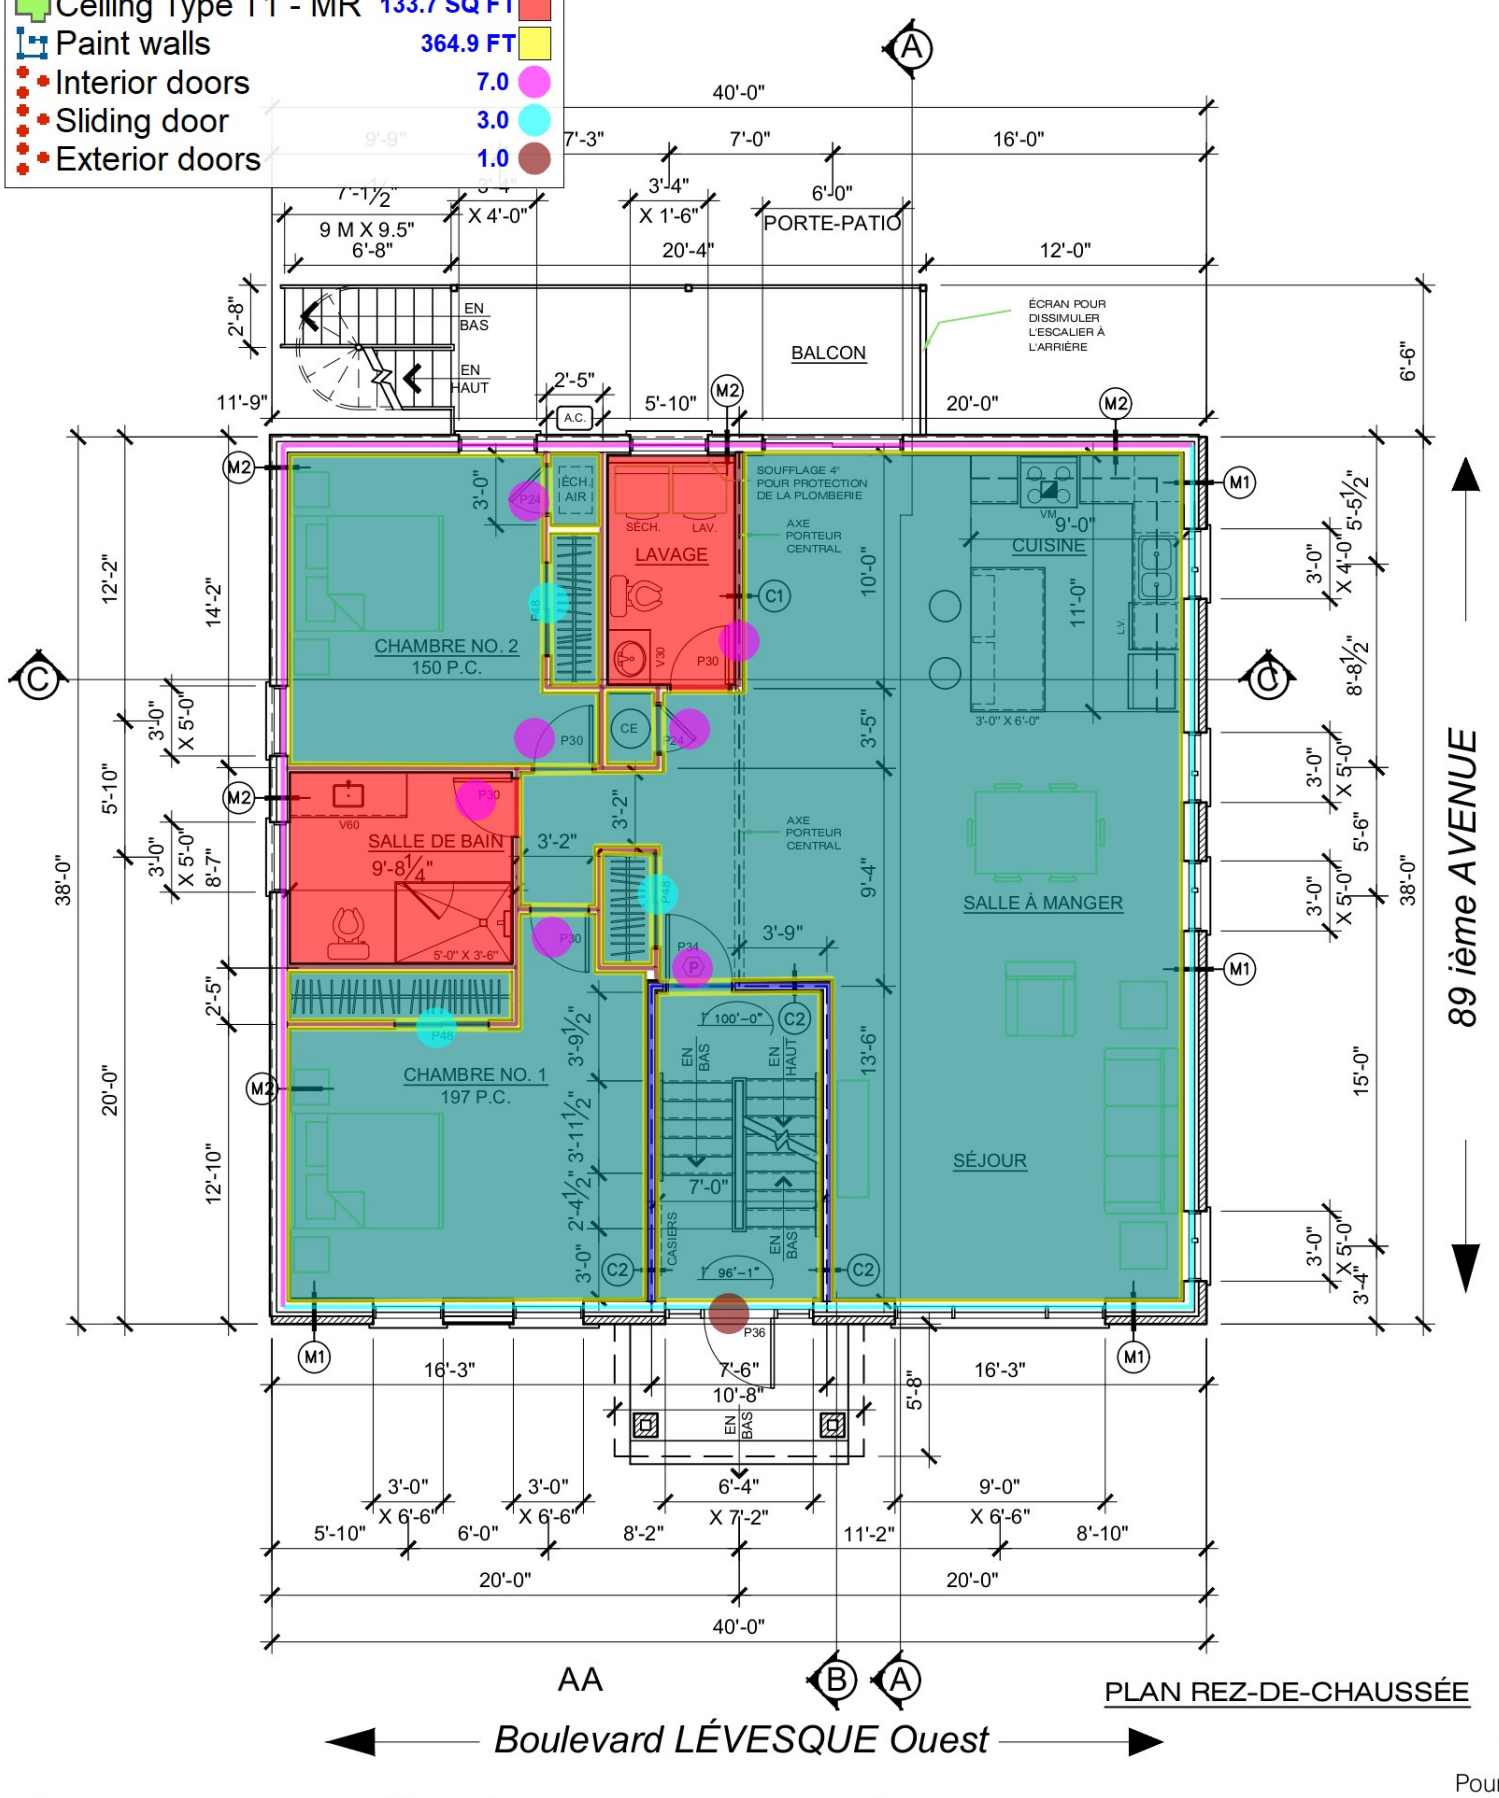

PLAN REZ-DE-CHAUSSÉE

NOTES DE L'ARCHITECTE:

- LES TRAVAUX CONSISTENT À CONSTRUIRE UNE NOUVELLE LOCATIF DE 4 LOGEMENTS DONT 2 AU SOUS–SOL.
- UN ARPENTEUR–GÉOMÈTRE DEVRA PRÉPARER UN PROJET D'IMPLANTATION ET SUPERVISER L'IMPLANTATION DU BATIMENT SUR LE SITE LORS DES TRAVAUX.
- LES EXIGENCES DU CHAPITRE 9 DU CODE NATIONAL DE CONSTRUCTION (ÉDITION QUÉBEC) S'APPLIQUENT À L'ENSEMBLE DES TRAVAUX.
- TOUS LES TRAVAUX DEVRONT ÉGALEMENT RESPECTER LES EXIGENCES DE LA VILLE DE LAVAL.
- LES DIMENSIONS DEVRONT ETRE VÉRIFIÉES SUR PLACE AVANT LE DÉBUT DES TRAVAUX. AVISER L'ARCHITECTE DE TOUTE DIFFÉRENCE.
- DES AVERTISSEURS DE FUMÉE ÉLECTRIQUES (INTER–RELIÉS ENTRE EUX) DEVRONT ETRE INSTALLÉS DANS CHACUNE DES CHAMBRES EN CONFORMITÉ AVEC LES EXIGENCES DU CODE DE CONSTRUCTION.
- UNE ATTENTION PARTICULIÈRE DEVRA ETRE APPORTÉE À L'ÉTANCHÉITÉ DU BATIMENT ET À SA VENTILATION AFIN D'ÉVITER TOUT PROBLÈME LIÉ À L'HUMIDITÉ.
- CHAQUE LOGEMENT DEVRA ETRE POURVU D'UN ÉCHANGEUR D'AIR AVEC RÉCUPÉRATEUR DE CHALEUR. CES EQUIPEMENTS DEVRONT ETRE SITUÉ SOUS LES GYSPE DES PLAFONDS AFIN D'ASSURER L'INTÉGRITÉ AU FEU DES ASSEMBLAGES.
- UN INGÉNIEUR EN STRUCTURE DEVRA ETRE ENGAGÉ POUR PRÉPARER LES PLANS DE CHARPENTE. NE PAS DÉBUTER LES TRAVAUX AVANT QUE CES PLANS SOIENT SCELLÉS ET SIGNÉE POUR CONSTRUCTION PAR L'INGÉNIEUR.
- UN INGÉNIEUR CIVIL DEVRA ETRE ÉGALEMENT MANDATÉ AFIN DE PRÉPARER LES PLANS DE DRAINAGE DU TERRAIN DONT LE STATIONNEMENT SITUÉ À L'ARRIÈRE EN CONTREBAS.
- AVANT DE DÉBUTER LES TRAVAUX L'ENTREPRENEUR DEVRA VÉRIFIER MINUTIEUSEMENT TOUS LES NIVEAUX DE TERRAIN ET INFORMER L'ARCHITECTE S'IL DÉTECTE DES PROBLÈMES POTENTIELS (DRAINAGE DU TERRAIN). DANS LE DOUTE IL DEVRA CONSULTER L'ARPENTEUR–GÉOMÈTRE.

A.C. UNITÉ DE CLIMATISATION (+ CHAUFFAGE)

17-07-2025
Pour Approbation Seulement

MARIO DUCHESNE
architecte
90, 83e Avenue
Montréal, QC
H1A 5H8
mario.duchesne.architecte@gmail.com
tel : 514 - 234 4497

PROJET:
Construction d'un Quadruplex
Lot 1 441 937
M. Claude Nabih Skaf 514 883 1783
4158 Boul. Lévesque Ouest
Laval, QC

DESSIN:
Plan du
REZ-DE-CHAUSSÉE

DESSINÉ PAR:	M.D.	NO.
VÉRIFIÉ PAR:	M.D.	A-02
ÉCHELLE:	1/8" = 1'-0"	
DATE:	04-08-2024	
DOSSIER:	MD24119	

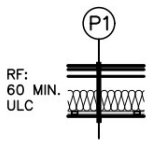

PLANCHER –P1–
FINI DE PLANCHER (PROPR.)
BÉTON LÉGER 1.5 po.
COUSSIN CAOUTCHOUC
C.P. 5/8" COLLÉ/FIXÉ
SOLIVES DE PLANCHER
PRÉFABRIQUÉES 12" NOM.
AVEC LAINE ROXUL 4"
BARRES RÉSILIENTES
2 X GYPSE 5/8" TYPE "X"

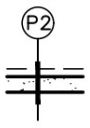

PLANCHER –P2–
FINI DE PLANCHER
(PROPRIÉTAIRE)
C.P. 5/8" COLLÉ/FIXÉ
FOURRURES 2" X 3" @ 16"
À PLAT
DALLE DE BÉTON ARMÉE
PARE–VAPEUR 6 MILS
STYROFOAM SM 1 po.
CONCASSÉ EXEMPT DE
PYRITE
SOL NATUREL SAIN

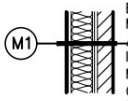

MUR –M1– (BRIQUES)
PAREMENT DE BRIQUES
ESPACE D'AIR 1"
MEMBRANE TYVEK
AGGLOMÉRÉ 7/16" AVEC
ISOLANT RIGIDE R4.
MONTANTS 2" X 6" @ 16"
C/C AVEC ISOLANT R20
PARE–VAPEUR 6 MILS
FOURRURES 1" X 3" @
16"C/C
GYPSE 5/8" TYPE "X"

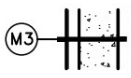

MUR –M3– FONDATION
GYPSE 5/8" F.C.
PARE–VAPEUR 6 MILS
MONTANTS 2" X 4" @ 16"
C/C AVEC LAINE R12
ISOLANT RIGIDE 1 po.
MUR DE BÉTON 10" OU 8"
IMPERMÉABILISÉ SOUS LE
SOL
ARMÉ 2 BARRES 10M HAUT
+ BAS DU MUR (VOIR ING.
TOUT LE PÉRIMÈTRE)

PORTE D'ENTRÉE LOGEMENTS
PORTE 20 MINUTES ULC
AVEC FERME–PORTES

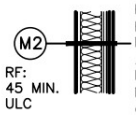

MUR –M2– (BARDAGE)
PAREMENT "CANEXEL"
FOURRURES DE BOIS 1"
MEMBRANE TYVEK
AGGLOMÉRÉ 7/16" AVEC
ISOLANT RIGIDE 1 po.
MONTANTS 2" X 6" @ 16"
C/C AVEC ISOLANT R20
PARE–VAPEUR 6 MILS
FOURRURES 1" X 3" @
16"C/C
GYPSE 5/8" TYPE "X"

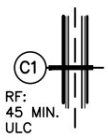

CLOISON –C1– CLOISONS PORTANTE
GYPSE 5/8" TYPE "X" F.C.
MONTANTS 2" X 4" @ 12"/16" C/C
AVEC LAINE ROXUL
GYPSE 5/8" TYPE "X" FC

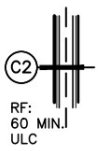

CLOISON –C2– CLOISONS ESCALIER
2 X GYPSE 5/8" TYPE "X" F.C.
MONTANTS 2" X 4" @ 12"/16" C/C
AVEC LAINE ROXUL
BARRES RÉSILIENTES ¾"
GYPSE 5/8" TYPE "X" FC

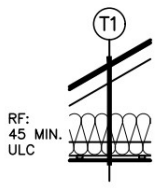

TOIT –T1–
BARDEAUX D'ASPHALTE 25
ANS SUR MEMBRANE
SOUS–COUCHE COLLÉE
SOPREMA
C.P. 5/8"
FERMES DE TOITURE
PRÉFABRIQUÉES AVEC ISOLANT
R40
NB: ENTRETOIT À VENTILER
AVEC DES AÉRATEURS
"MAXIMUM"
PARE–VAPEUR 6 MILS
FOURRURES 1" X 3" @ 16"C/C
1 X GYPSE 5/8" TYPE "X"

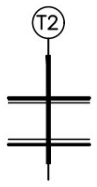

TOIT –T2–
MEMBRANE ÉLASTOMÈRE
SOPREMA
SOUS–COUCHE (BASE) SOPREMA
C.P. 3/4" EMBOUVETÉ
POUTRELLES DE TOITURE
PRÉFABRIQUÉES
NB: ENTRETOIT À VENTILER PAR
EN DESSOUS
FOURRURES DE BOIS
SOFFITE (VENTILÉ)

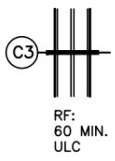

CLOISON –C3– DOUBLE
GYPSE 5/8" TYPE "X" FC
BARRES RÉSILIENTES
MONTANTS 2" X 6" @ 12"/16" C/C
AVEC LAINE INSONORISANTE
ESPACE D'AIR 3/4"
MONTANTS 2" X 4" @ 12"/16" C/C
AVEC LAINE INSONORISANTE
BARRES RÉSILIENTES
GYPSE 5/8" TYPE "X" FC

ASSEMBLAGES TYPIQUES

Type M2	75.9 FT
Type M1	75.9 FT
Type C2	34.6 FT
Type C1	110.6 FT
Ceiling Type P1	1,137.8 SQ FT
Ceiling Type P1 - MR	133.6 SQ FT
Paint walls	352.2 FT
Interior doors	6.0
Sliding door	3.0

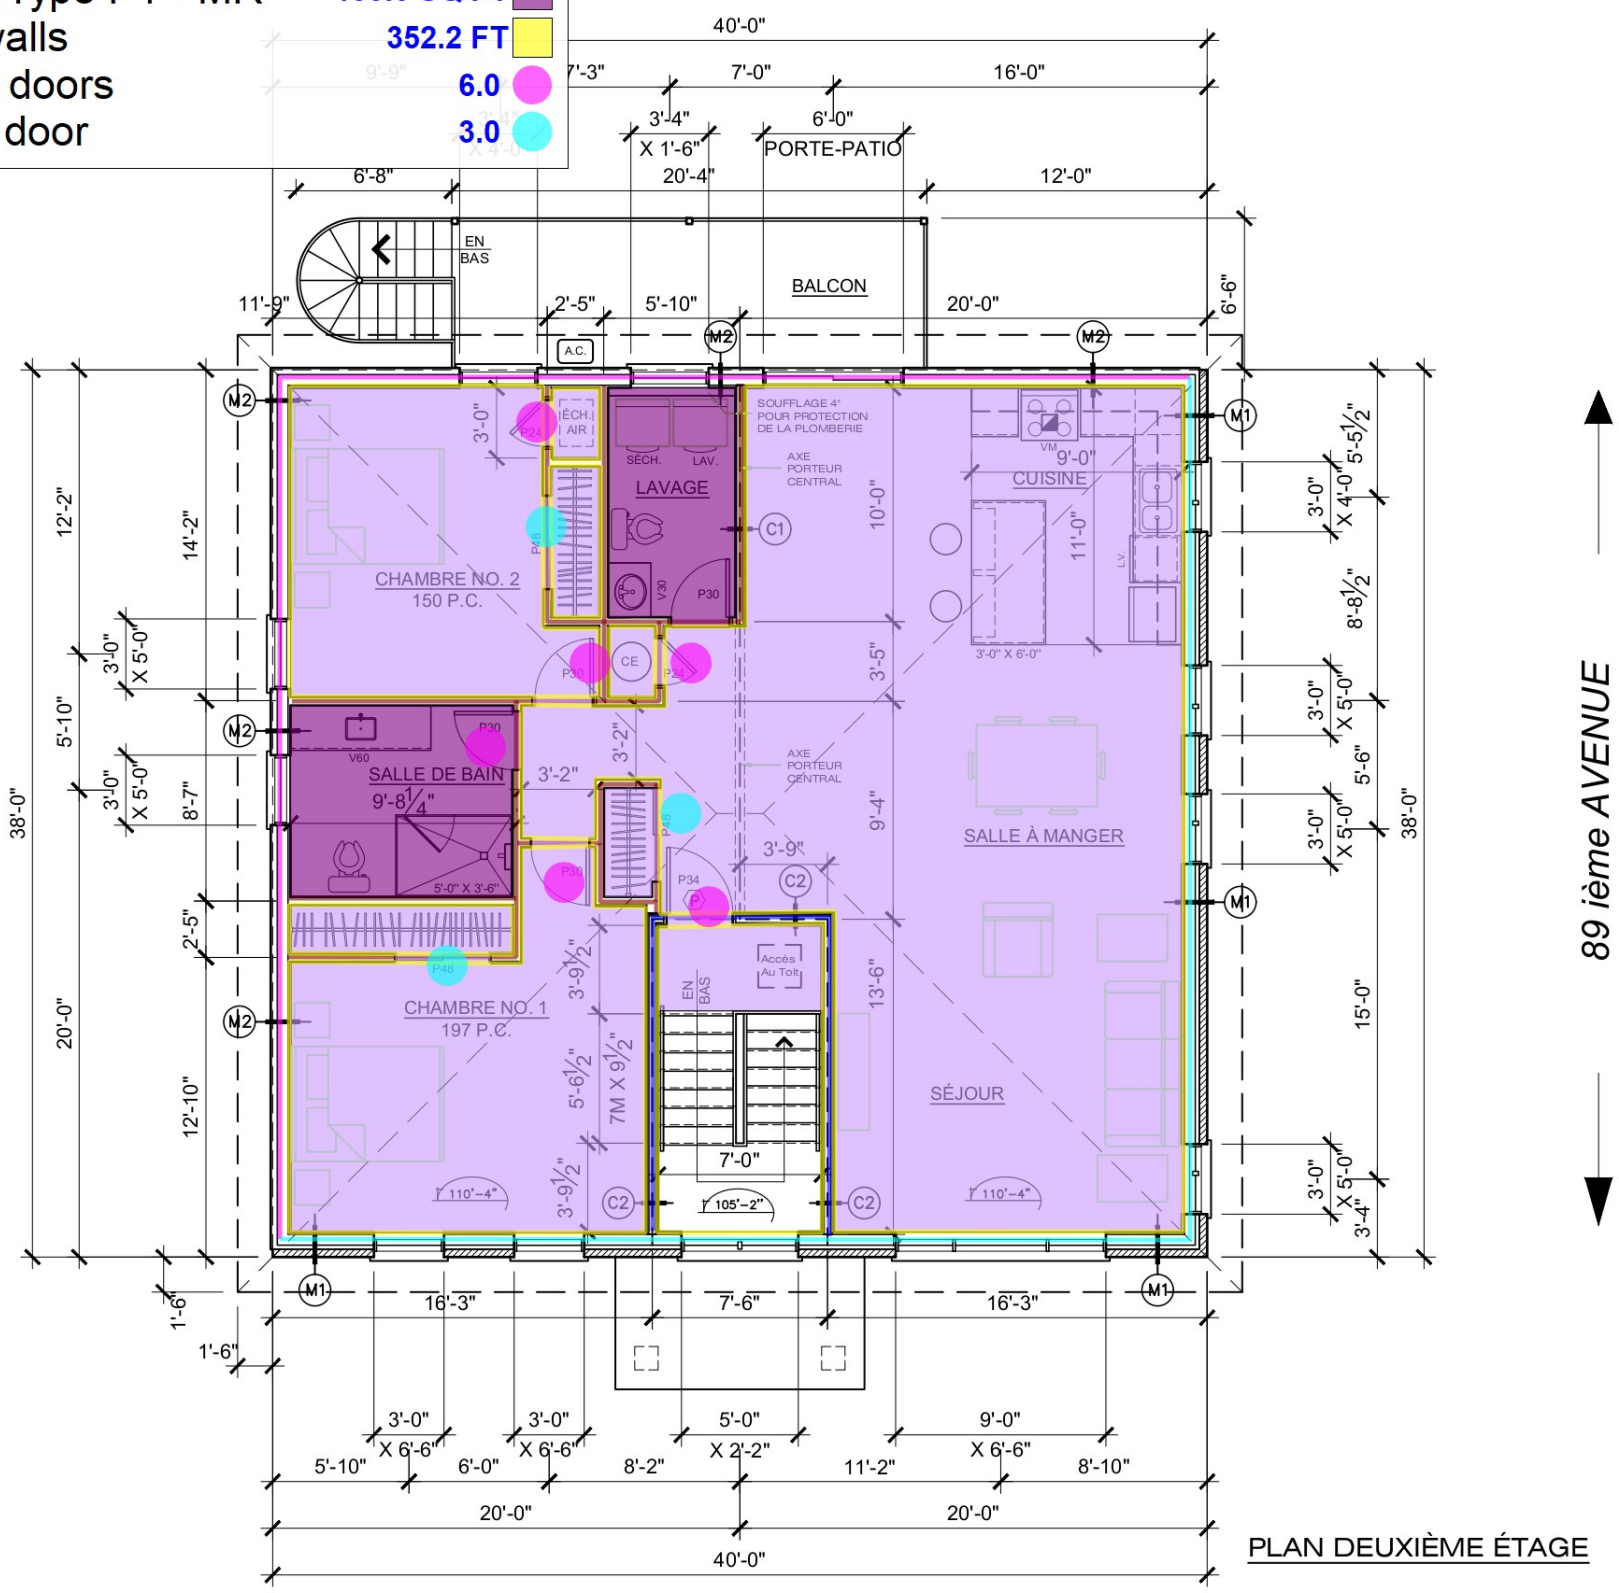

PLAN DEUXIÈME ÉTAGE

89 ième AVENUE

Boulevard LÉVESQUE Ouest

17-07-2025
Pour Approbation Seulement

MARIO DUCHESNE
architecte
90, 83e Avenue
Montréal, QC
H1A 5H8
mario.duchesne.architecte@gmail.com
tel : 514 - 234 4497

PROJET:
Construction d'un Quadruplex
Lot 1 441 937
M. Claude Nabih Skaf 514 883 1783
4158 Boul. Lévesque Ouest
Laval, QC

DESSIN:
Plan du
DEUXIÈME ÉTAGE

DESSINÉ PAR:	M.D.	NO.
VÉRIFIÉ PAR:	M.D.	A-03
ÉCHELLE:	1/8" = 1'-0"	
DATE:	04-08-2024	
DOSSIER:	MD24119	

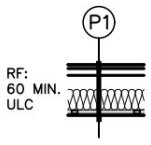

PLANCHER –P1–
FINI DE PLANCHER (PROPR.)
BÉTON LÉGER 1.5 po.
COUSSIN CAOUTCHOUC
C.P. 5/8" COLLÉ/FIXÉ
SOLIVES DE PLANCHER
PRÉFABRIQUÉES 12" NOM.
AVEC LAINE ROXUL 4"
BARRES RÉSILIENTES
2 X GYPSE 5/8" TYPE "X"

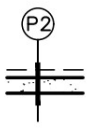

PLANCHER –P2–
FINI DE PLANCHER
(PROPRIÉTAIRE)
C.P. 5/8" COLLÉ/FIXÉ
FOURRURES 2" X 3" @ 16"
À PLAT
DALLE DE BÉTON ARMÉE
PARE–VAPEUR 6 MILS
STYROFOAM SM 1 po.
CONCASSÉ EXEMPT DE
PYRITE
SOL NATUREL SAIN

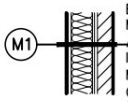

MUR –M1– (BRIQUES)
PAREMENT DE BRIQUES
ESPACE D'AIR 1"
MEMBRANE TYVEK
AGGLOMÉRÉ 7/16" AVEC
ISOLANT RIGIDE R4.
MONTANTS 2" X 6" @ 16"
C/C AVEC ISOLANT R20
PARE–VAPEUR 6 MILS
FOURRURES 1" X 3" @
16"C/C
GYPSE 5/8" TYPE "X"

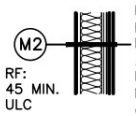

MUR –M2– (BARDAGE)
PAREMENT "CANEXEL"
FOURRURES DE BOIS 1"
MEMBRANE TYVEK
AGGLOMÉRÉ 7/16" AVEC
ISOLANT RIGIDE 1 po.
MONTANTS 2" X 6" @ 16"
C/C AVEC ISOLANT R20
PARE–VAPEUR 6 MILS
FOURRURES 1" X 3" @
16"C/C
GYPSE 5/8" TYPE "X"

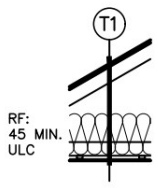

TOIT –T1–
BARDEAUX D'ASPHALTE 25
ANS SUR MEMBRANE
SOUS–COUCHE COLLÉE
SOPREMA
C.P. 5/8"
FERMES DE TOITURE
PRÉFABRIQUÉES AVEC ISOLANT
R40
NB: ENTRETOIT À VENTILER
AVEC DES AÉRATEURS
"MAXIMUM"
PARE–VAPEUR 6 MILS
FOURRURES 1" X 3" @ 16"C/C
1 X GYPSE 5/8" TYPE "X"

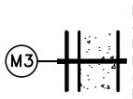

MUR –M3– FONDATION
GYPSE 5/8" F.C.
PARE–VAPEUR 6 MILS
MONTANTS 2" X 4" @ 16"
C/C AVEC LAINE R12
ISOLANT RIGIDE 1 po.
MUR DE BÉTON 10" OU 8"
IMPERMÉABILISÉ SOUS LE
SOL
ARMÉ 2 BARRES 10M HAUT
+ BAS DU MUR (VOIR ING.
TOUT LE PÉRIMÈTRE)

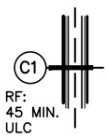

CLOISON –C1– CLOISONS PORTANTE
GYPSE 5/8" TYPE "X" F.C.
MONTANTS 2" X 4" @ 12"/16" C/C
AVEC LAINE ROXUL
GYPSE 5/8" TYPE "X" FC

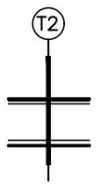

TOIT –T2–
MEMBRANE ÉLASTOMÈRE
SOPREMA
SOUS–COUCHE (BASE) SOPREMA
C.P. 3/4" EMBOUVETÉ
POUTRELLES DE TOITURE
PRÉFABRIQUÉES
NB: ENTRETOIT À VENTILER PAR
EN DESSOUS
FOURRURES DE BOIS
SOFFITE (VENTILÉ)

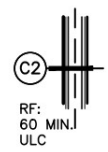

CLOISON –C2– CLOISONS ESCALIER
2 X GYPSE 5/8" TYPE "X" F.C.
MONTANTS 2" X 4" @ 12"/16" C/C
AVEC LAINE ROXUL
BARRES RÉSILIENTES
GYPSE 5/8" TYPE "X" FC

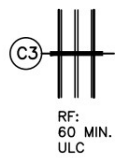

CLOISON –C3– DOUBLE
GYPSE 5/8" TYPE "X" FC
BARRES RÉSILIENTES
MONTANTS 2" X 6" @ 12"/16" C/C
AVEC LAINE INSONORISANTE
ESPACE D'AIR 3/4"
MONTANTS 2" X 4" @ 12"/16" C/C
AVEC LAINE INSONORISANTE
BARRES RÉSILIENTES
GYPSE 5/8" TYPE "X" FC

PORTE D'ENTRÉE LOGEMENTS
PORTE 20 MINUTES ULC
AVEC FERME–PORTES

ASSEMBLAGES TYPIQUES

Type M3	152.4 FT
Type C2	34.2 FT
Type C3	22.6 FT
Type C1	117.4 FT
Ceiling Type P1	1,084.3 SQ FT
Ceiling Type P1 - MR	112.0 SQ FT
Paint walls	379.6 FT
Interior doors	4.0
Sliding door	4.0

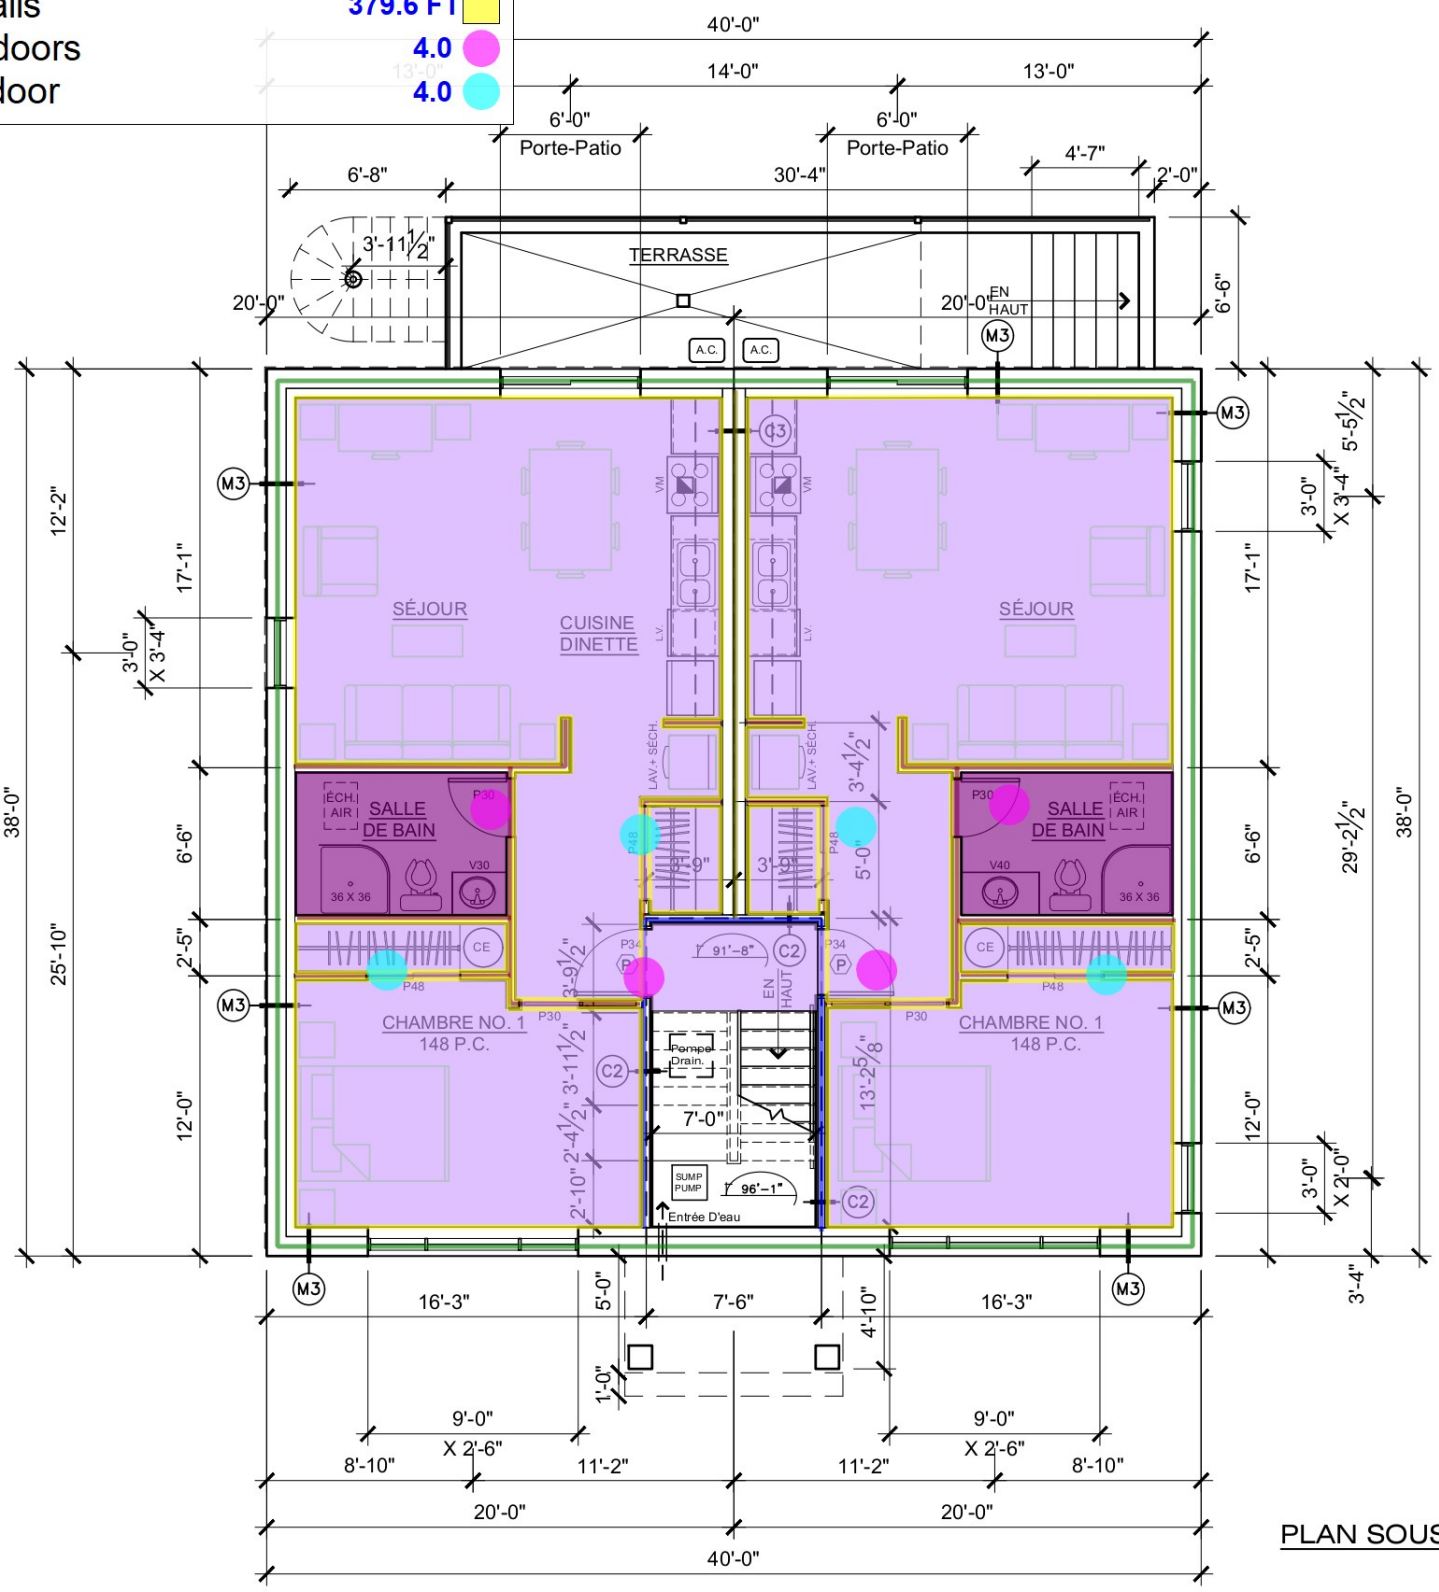

PLAN SOUS-SOL

Boulevard LÉVESQUE Ouest

17-07-2025
Pour Approbation Seulement

MARIO DUCHESNE
architecte
90, 83e Avenue
Montréal, QC
H1A 5H8
mario.duchesne.architecte@gmail.com
tel : 514 - 234 4497

PROJET:
Construction d'un Quadruplex
Lot 1 441 937
M. Claude Nabih Skaf 514 883 1783
4158 Boul. Lévesque Ouest
Laval, QC

DESSIN:
Plan du
SOUS-SOL

DESSINÉ PAR:	M.D.	NO.
VÉRIFIÉ PAR:	M.D.	A-04
ÉCHELLE:	1/8" = 1'-0"	
DATE:	04-08-2024	
DOSSIER:	MD24119	